

SISTEMA DE NIVEL DE LIQUIDO

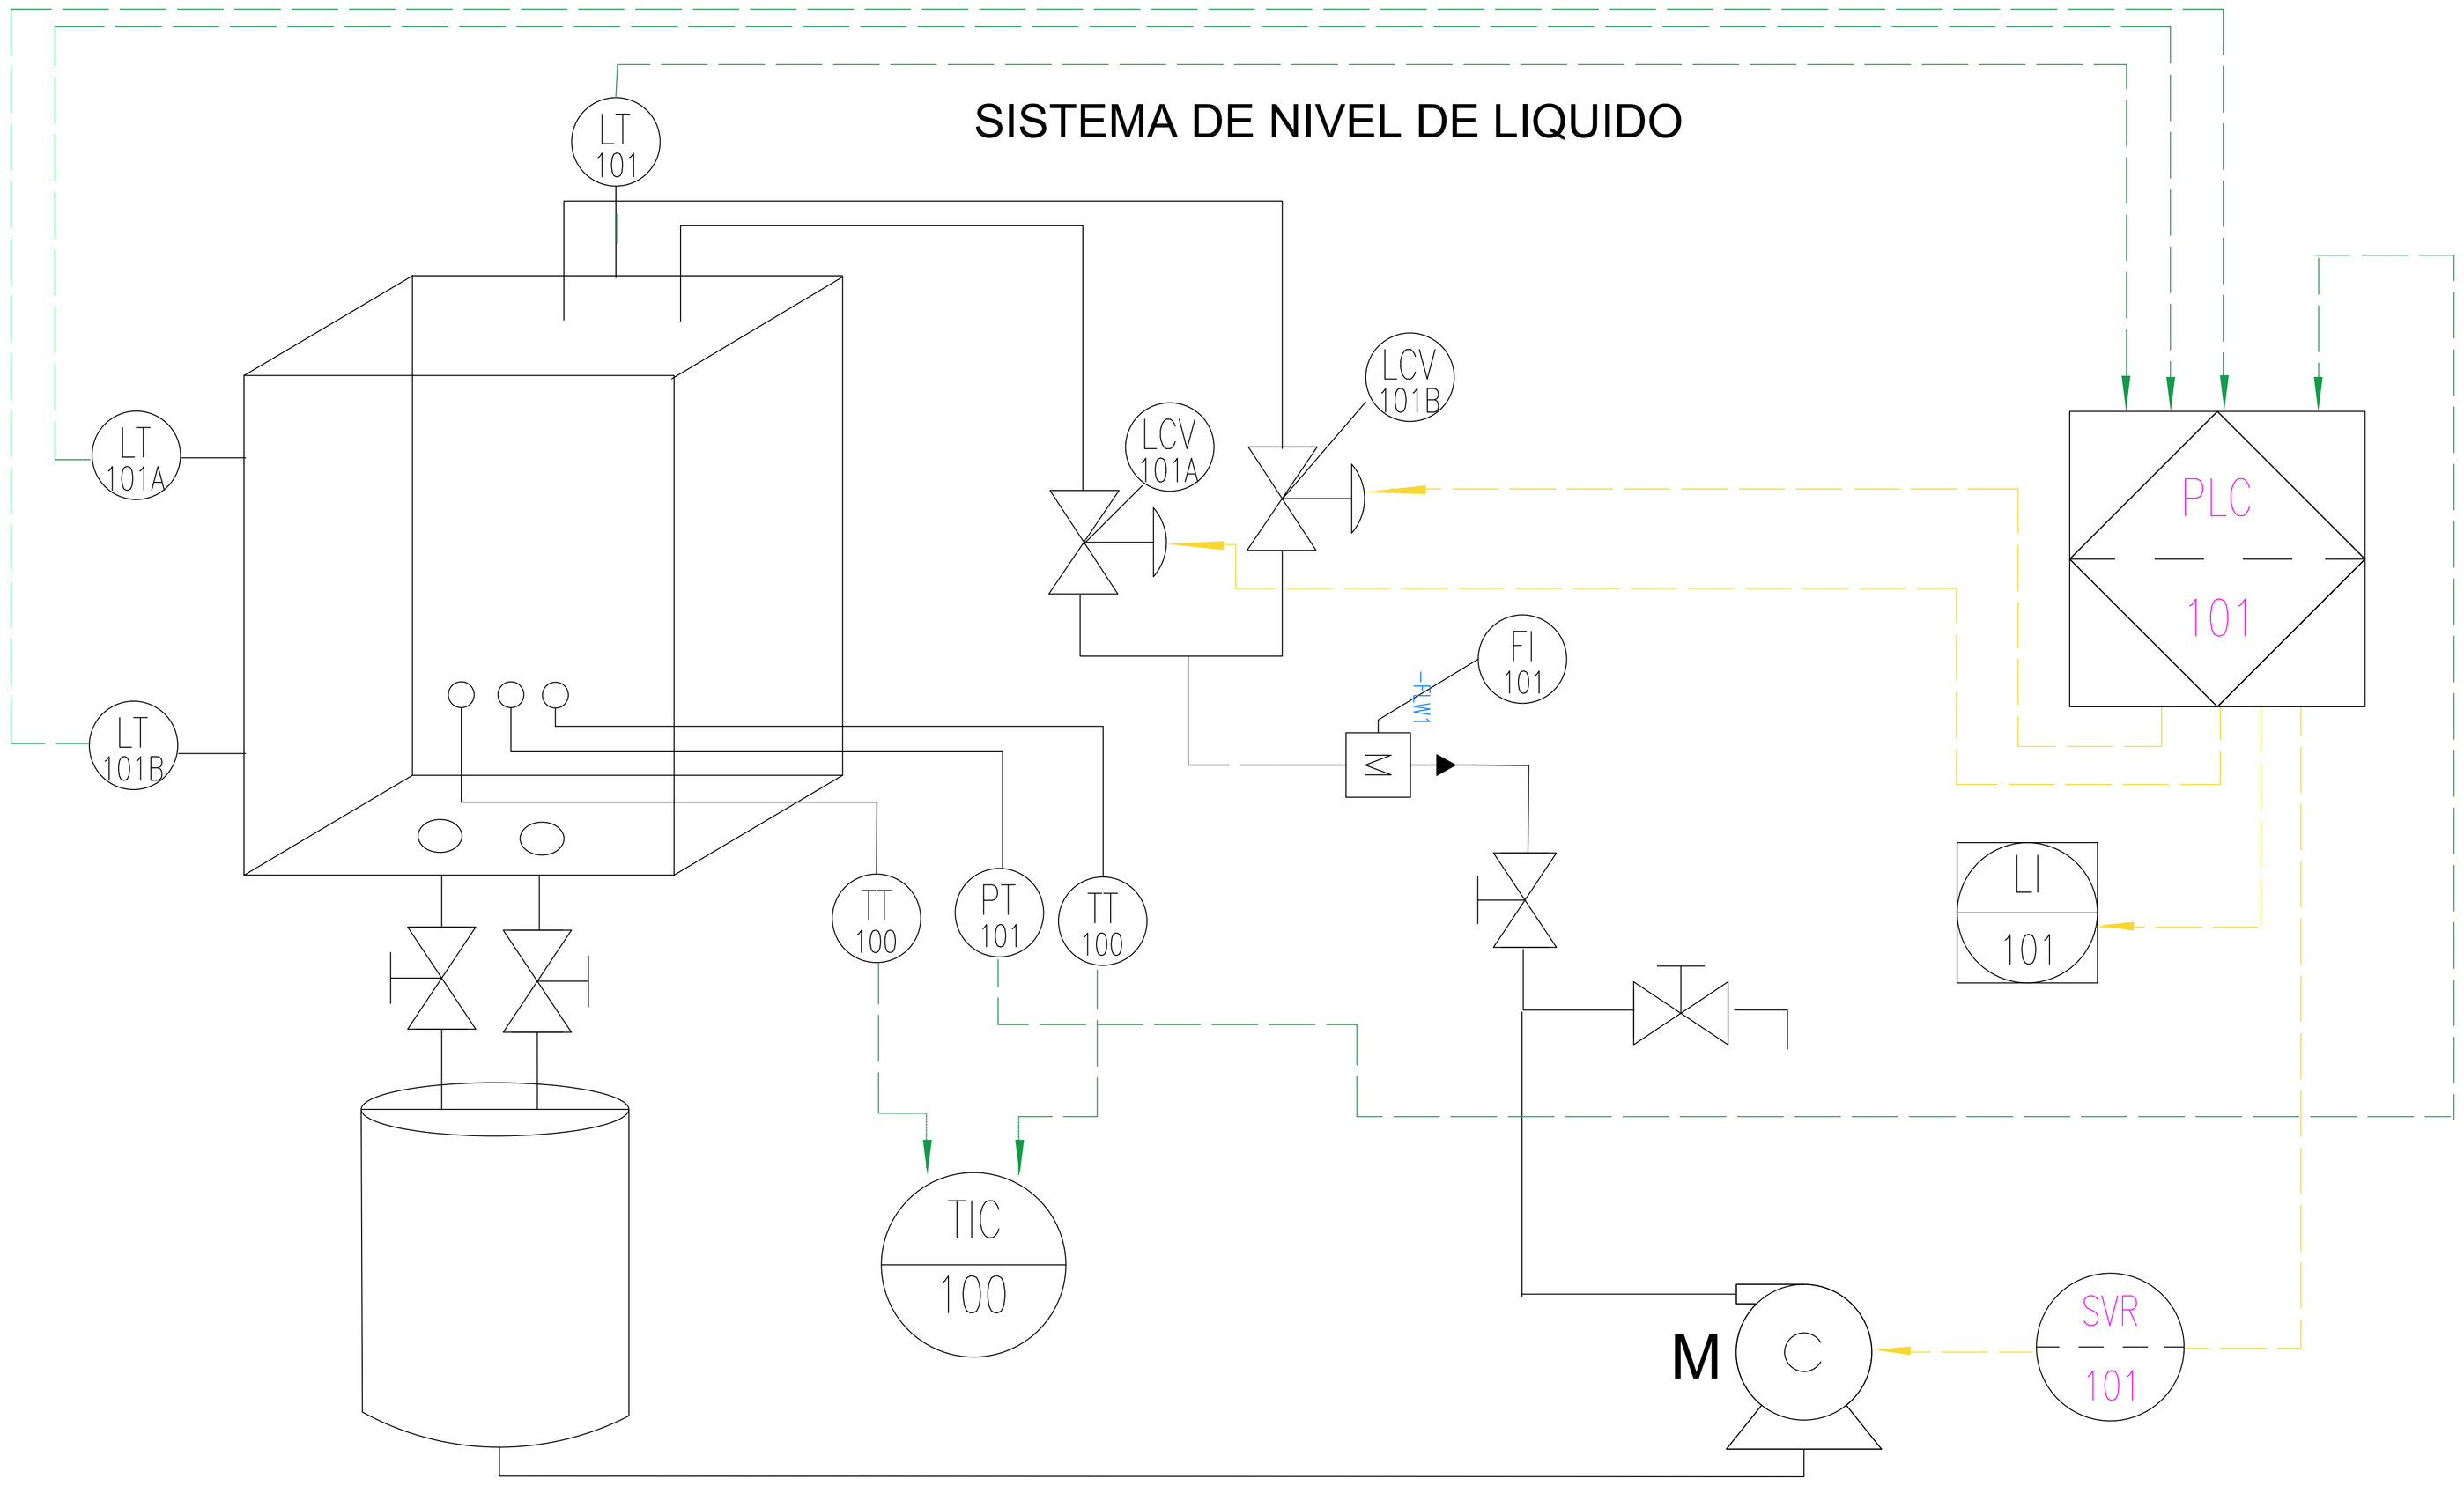

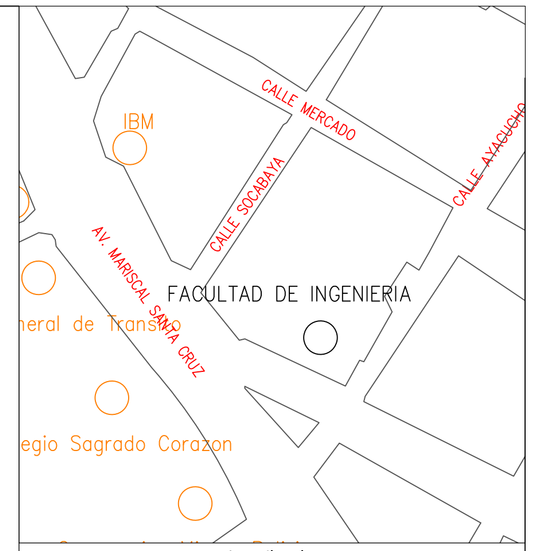

Localizacion

Notas

1.
2.

ELEMENTOS DEL SISTEMA

ITEM	ELEMENTOS DEL SISTEMA	DESCRIPCIÓN
1.	LT-101	TRANSMISOR DE NIVEL (ULTRASONICO)
2.	LT-101A	TRANSMISOR DE NIVEL ALTO
3.	LT101B	TRANSMISOR DE NIVEL BAJO
4.	LCV-101A	VÁLVULA DE CONTROL DE NIVEL 1
5.	LCV-101B	VÁLVULA DE CONTROL DE NIVEL 2
6.	FI-101	INDICADOR DE FLUJO
7.	LI-101	INDICADOR DE NIVEL
8.	PLC-101	CONTROLADOR LÓGICO PROGRAMABLE
9.	SVR-101	REGULADOR VARIADOR DE VELOCIDAD
10.	M	MOTOR BOMBA
11.	TT-100	TRANSMISOR DE TEMPERATURA 1
12	PT-101	TRANSMISOR DE PRESION
13	TT-101	TRANSMISOR DE TEMPERATURA 2
14	TIC-100	CONTROLADOR INDICADOR DE TEMPERATURA
15	VÁLVULAS MANUAL	ABRE Y CIERRA EL PASO DEL LIQUIDO
16	ELECTROVALVULAS	CONTROLA EL PASO DEL LIQUIDO POR LA TUBERIA
17	DOSIFICADOR	PARA MEDIR EL CAUDAL VOLUMÉTRICO DE LIQUIDO
18	LINEAS NEGRAS	LINEA PRINCIPAL DEL PROCESO
19	LINEAS SEGMENTADAS VERDE	ENTRADAS AL PLC
20	LINEAS SEGMENTADAS AMARRILLO	SALIDA DEL PLC

Rev	Fecha	Emitido para	Dibujó	Diseñó	Revisó	Aprobó
A	xxxxxxxxx	Emitido para revisión	xxxxxx	xxxxxxx	xxxxxx	xxxx

Revisiones

Cliente

INGENIERIA ELECTRONICA

Consultor

ING. Jorge Antonio Nava Amador

Nombre De Proyecto

SISTEMA DE NIVEL

Tipo de plano: DIAGRAMA P&ID

FECHA: 10/10/2023

ASIGNATURA: ETN - 1034

ESCALA: 1:10

DIRIGIDO PARA: Dirigido para revision

Revisó auxiliar:	CRISTHIAN APAZA FLORES	Matrícula:	1760027	Firma:	
Revisó auxiliar:	KAREL GOMEZ ORELLANA	Matrícula:	1760036	Firma:	
Revisó Ingeniero:	JORGE ANTONIO NAVA AMADOR			Firma:	
dibujo:	Hanol Marlon Huanacu Condori	Matrícula:	1679381	Firma:	
	Guido Alvaro Laruta Poma	Matrícula:	1751542	Firma:	
	Williams Quispe Lucana	Matrícula:	1700862	Firma:	
	Edith Elvira Ramos Quelo	Matrícula:	1751560	Firma:	

NUMERO DE PLANO

2/4