
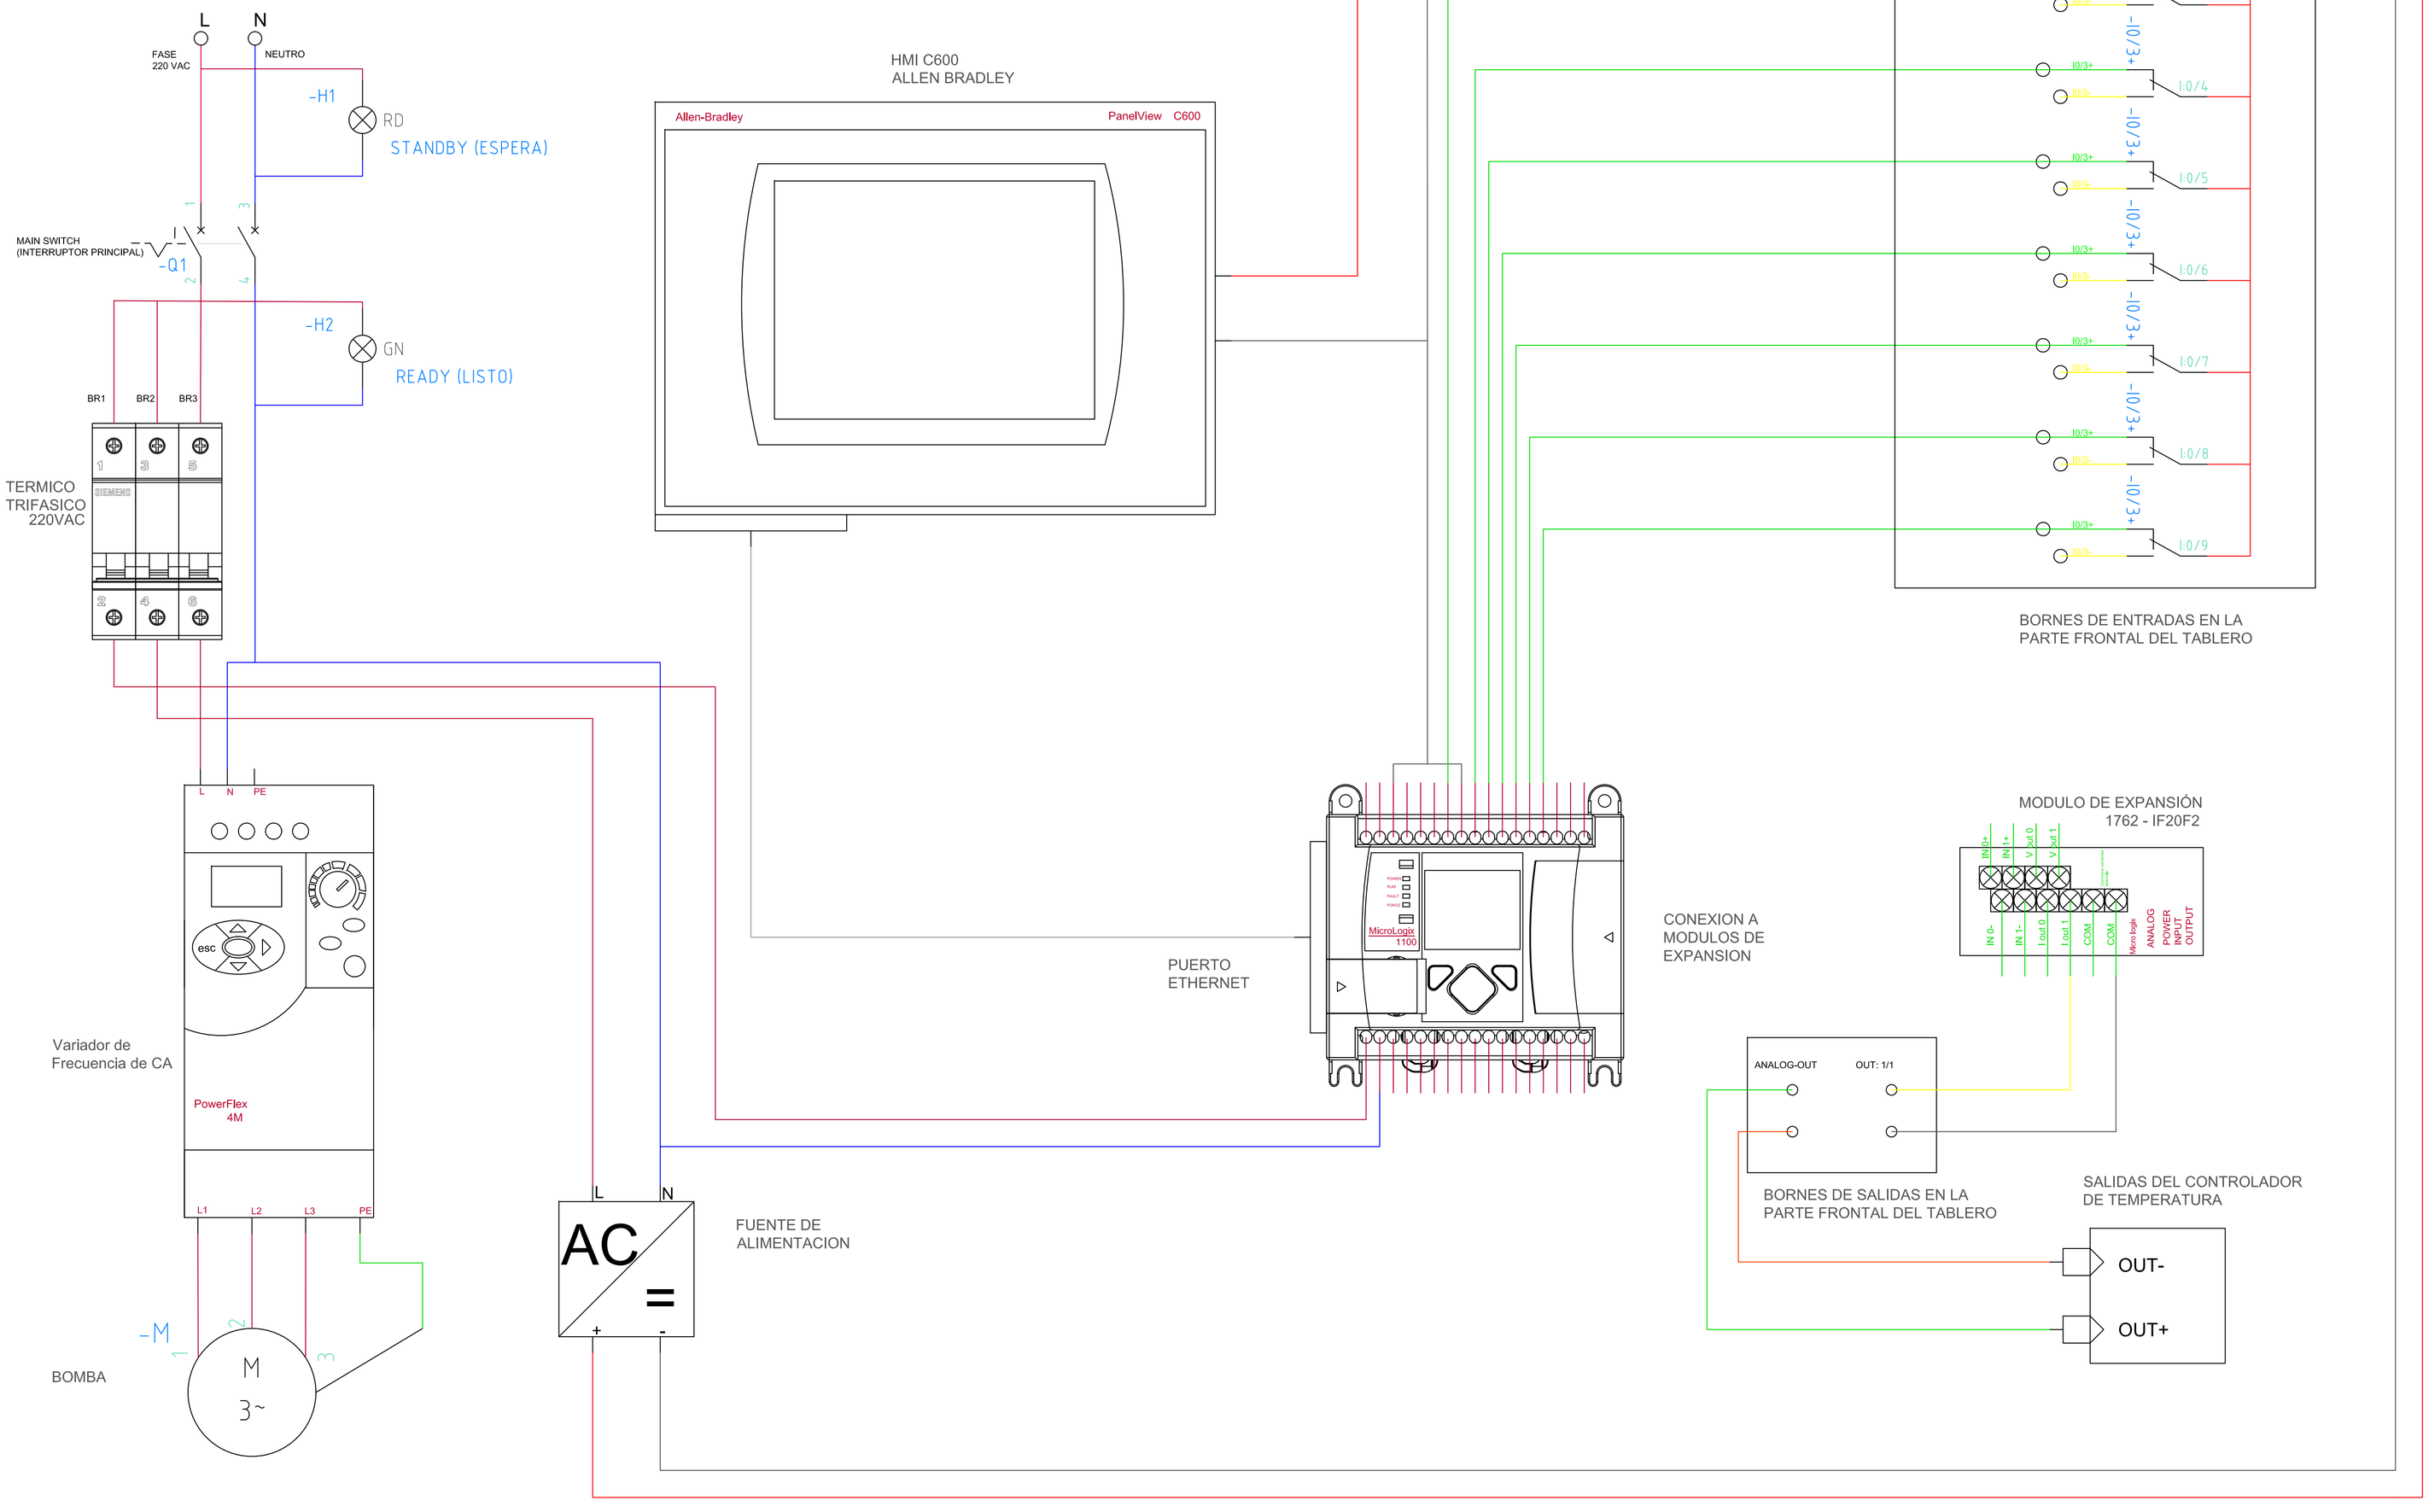


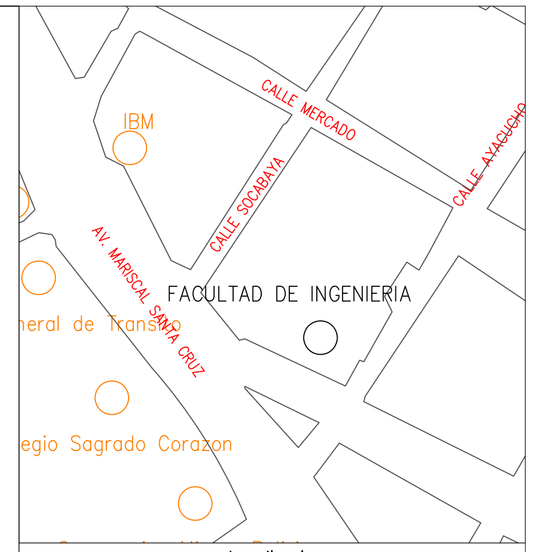

Localizacion

Notas

1.
2.

ELEMENTOS DEL SISTEMA

ITEM	ELEMENTOS DEL SISTEMA	DESCRIPCIÓN
1.	MAIN SWITCH	Interruptor principal de Inicio
2.	H1,H2	señalizacion de funcionamiento (ESPERA, LISTO)
3.	TERMICO TRIFASICO	trifásico de 220VAC
4.	VARIADOR DE FRECUENCIA	Regula la frecuencia de la electricidad que recibe el motor
5.	MOTOR	actuador encargado de llevar el liquido
6.	PLC	Se encarga de recibir las señales analógicas del nivel del tanque
7.	HMI C600	visualizador de medidas escaladas por el plc
8.	CONTROLADOR DE TEMPERATURA	indicador de temperatura
9.		
10.		
11.		

Rev	Fecha	Emitido para	Dibujó	Diseñó	Revisó	Aprobó
A	xxxxxxxxx	Emitido para revisión	xxxxxx	xxxxxxx	xxxxxx	xxxx

Revisiones

Cliente

INGENIERIA ELECTRONICA

Consultor

ING. Jorge Antonio Nava Amador

Nombre De Proyecto

SISTEMA DE NIVEL

Tipo de plano

PANEL ELÉCTRICO

FECHA: 10/10/2023

ASIGNATURA: ETN - 1034	Revisó auxiliar:	CRISTHIAN APAZA FLORES	Matrícula:	1760027	Firma:	
	Revisó auxiliar:	KAROL GOMEZ ORELLANA	Matrícula:	1760036	Firma:	
ESCALA: 1:10	Revisó Ingeniero:	JORGE ANTONIO NAVA AMADOR			Firma:	
DIRIGIDO PARA: Dirigido para revision	dibujo:	Heydi Marilyn Huanacu Condori	Matrícula:	1679381	Firma:	
		Guido Alvaro Llanos Pinto	Matrícula:	1751842	Firma:	
		Williams Quispe Lucana	Matrícula:	1702662	Firma:	
		Edith Elvira Ramos Guebe	Matrícula:	1751860	Firma:	

NUMERO DE PLANO

3/4